



DESIGN VISION & CONCEPT

LUXURY CONTEMPORARY

ARCHITECTURAL DOCUMENTATION

PROJECT - VASANT KUNJ DDA RESIDENCE



indéva
Studio

DESIGN CONCEPT & MATERIAL MOODBOARD

PALETTE

Warm beige PU, natural walnut veneer, Calacatta marble, brushed brass

SURFACES

FlutedMDF panels, upholstered headboard, matte lacquer finishes

LIGHTING

3000K warm white, cove LEDs, brass wall sconces, pendant accents

A minimal, editorial narrative grounded in warm natural materials and precise architectural detailing.

PHILOSOPHY & MOOD

The Golden Walnut & Charcoal Retreat — Modern. Warm. Timeless.

LIGHTING STRATEGY

CONTINUOUS LED COVE

Warmwhite, dimmable, high CRI — perimeter cove defines the room's ambient luminance.


PANEL & RECESS LIGHTING


Fluted wood panel LED strip · Recessed linear wall guides · Recess bookplate LED strip

FEATURE & ACCENT

Adjustable spherical pendants · Integrated RGB/warm white backlighting · App-controlled zoning


LIGHTING PLAN

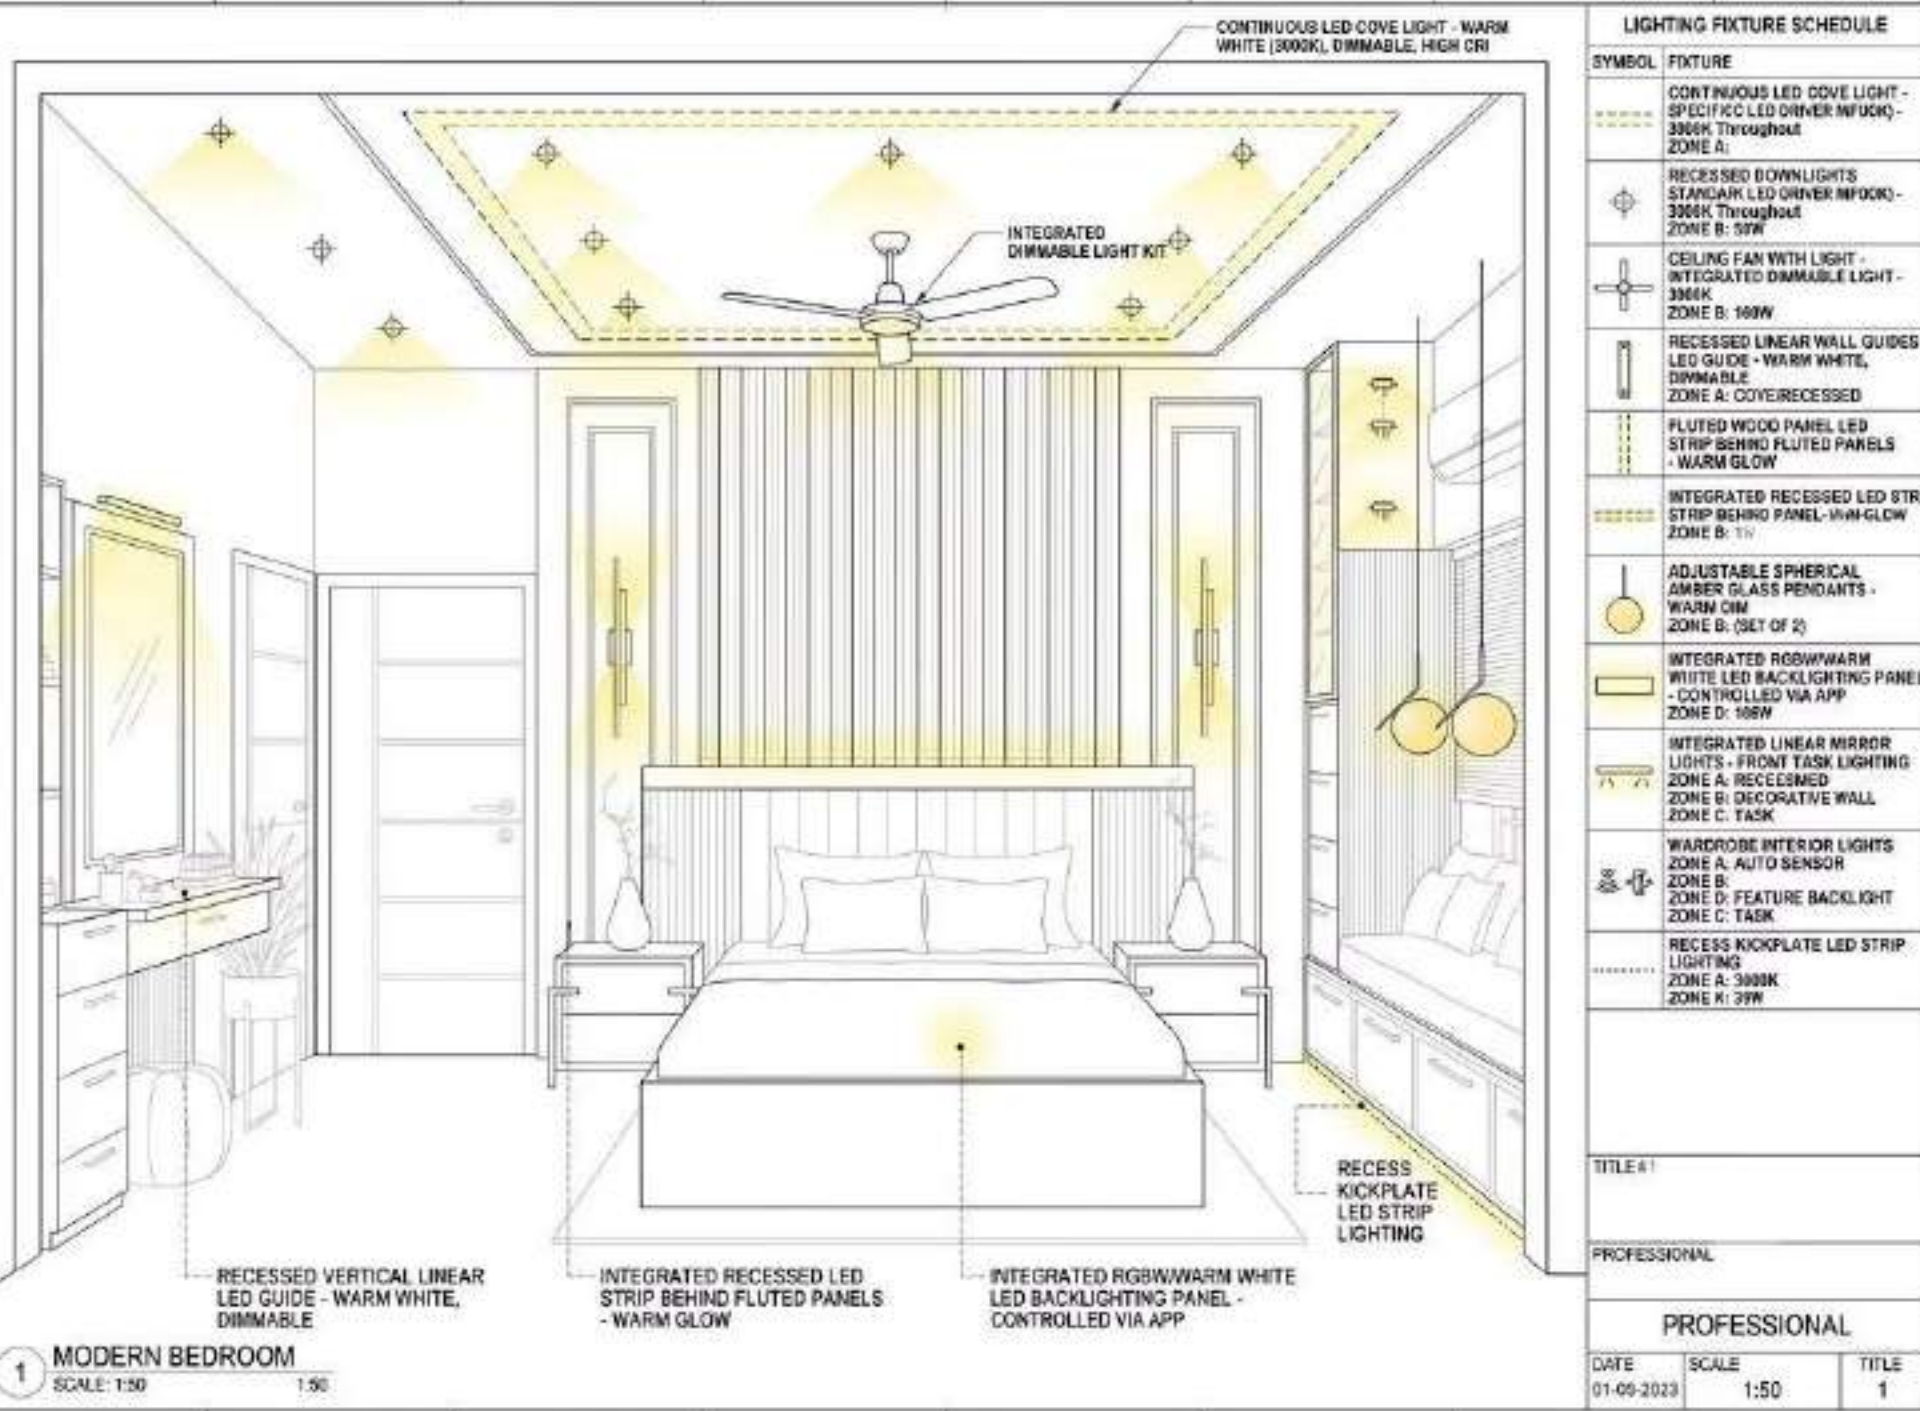

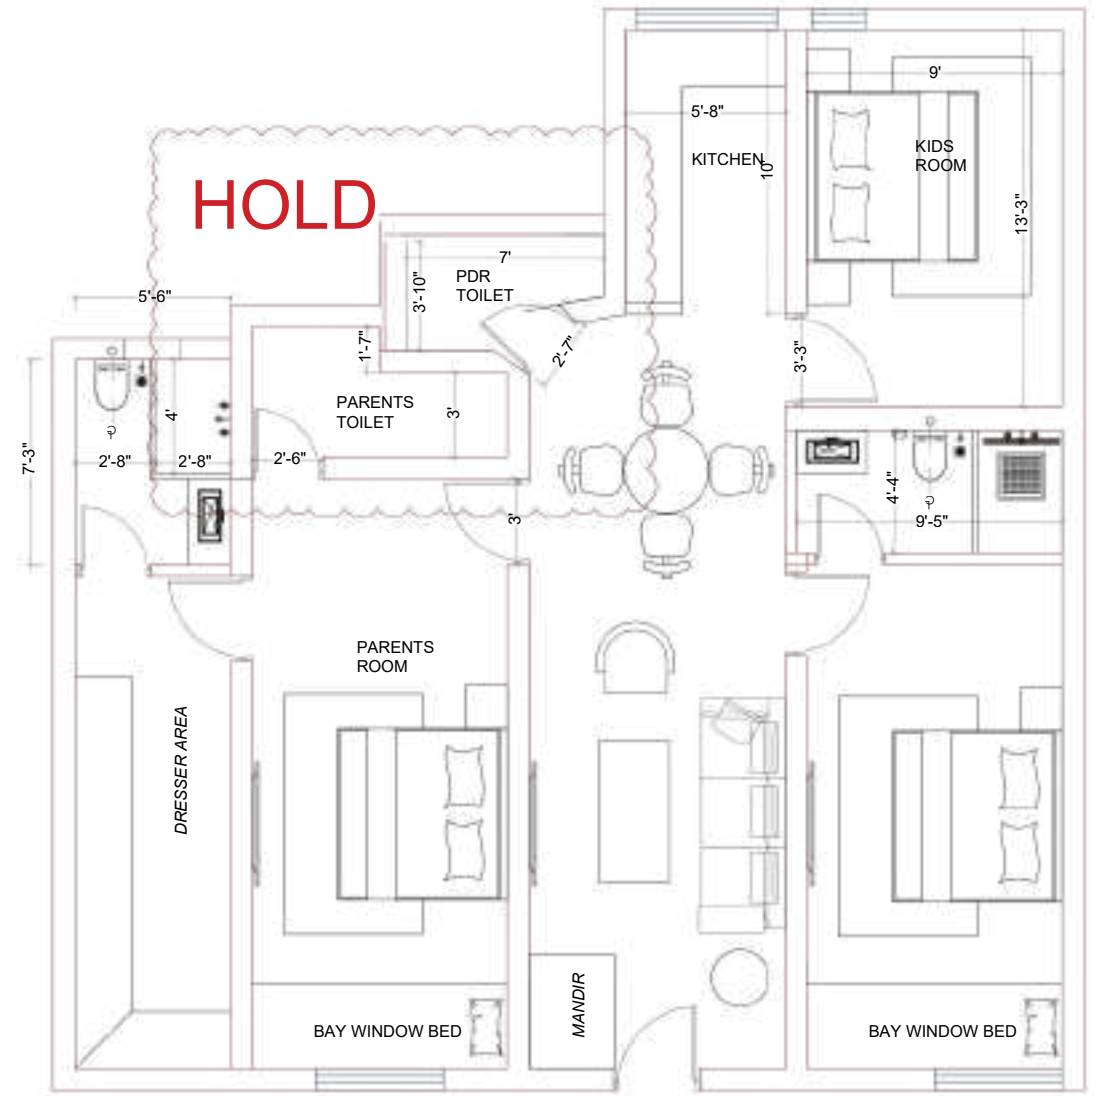

Floor Plan and Site Images of the Area

CEILING & LIGHTING LAYOUT

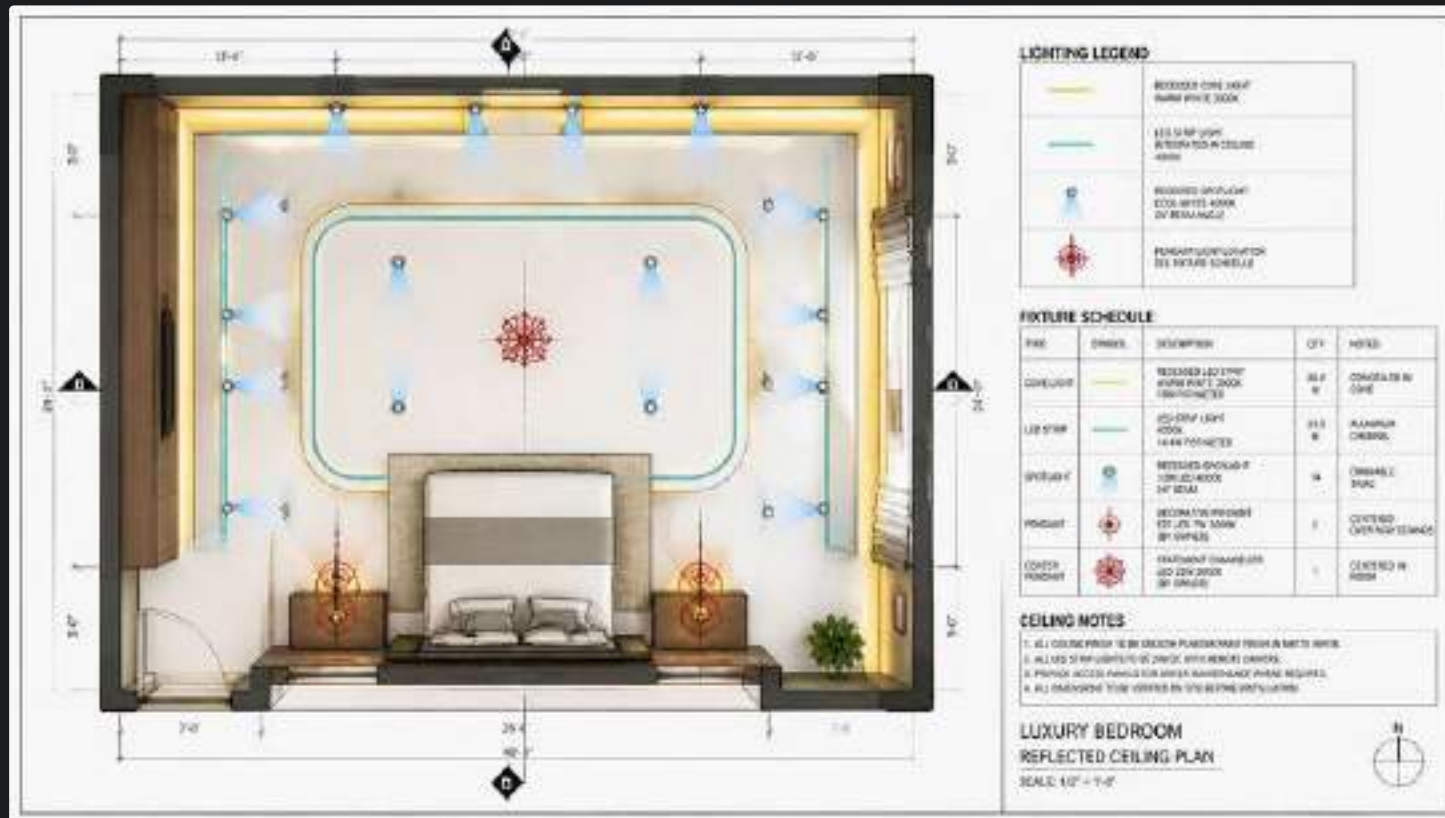

LIGHTING ZONES

- Cove lighting – perimeter, indirect wash
- Spotlights – 8 nos., 7W, 36° beam
- Wall sconces – bedside, brushed brass
- Pendants – dressing area, 2 nos.
- LED strips – headboard, TV unit, window seat

FIXTURE SCHEDULE

All fixtures 3000K warm white.
Dimmable circuits for ambient and task zones. Drivers concealed in ceiling void.

SPACE PLANNING

SPATIAL ZONING

ZONE A

Sleep & Rest—Centred bed, symmetrical flanking joinery, clear circulation path on both sides.

ZONE B

Dressing & Vanity — LED-lit mirror positioned for natural light adjacency.


ZONE C

Media & Entertainment — TV unit with recessed LED backlighting, app-controlled.

ZONE D

Reading & Relaxation — Window seat with built-in storage and soft upholstery.

SPATIAL ZONING PLAN: MODERN BEDROOM UNIT

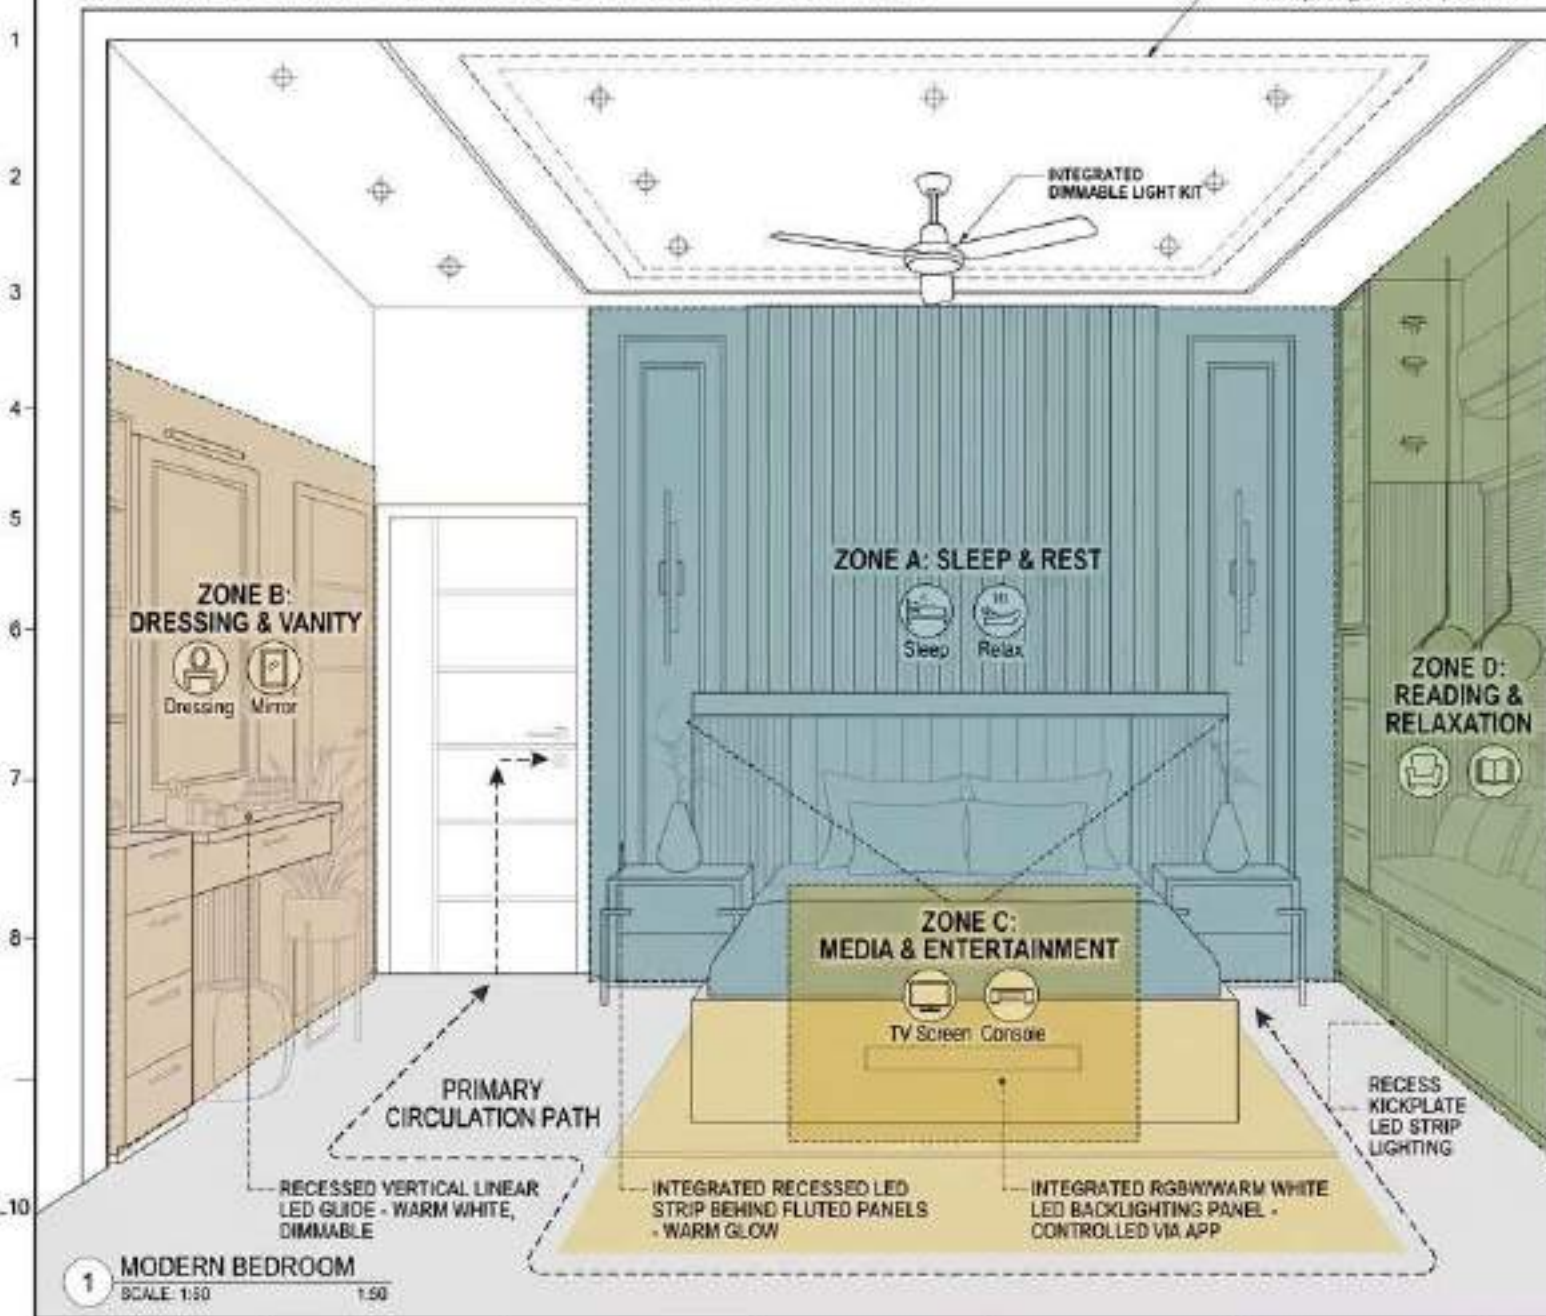

LIGHTING FIXTURE SCHEDULE		
SYMBOL	FIXTURE	
	CONTINUOUS LED COVE LIGHT - SPECIFIC LED DRIVER (MF00K) - 3500K Throughout ZONE A:	
	RECESSED DOWNLIGHTS STANCAK LED DRIVER (MF00K) - 3500K Throughout ZONE B: 50W	
	CEILING FAN WITH LIGHT - INTEGRATED DIMMABLE LIGHT - 3500K ZONE B: 160W	
	RECESSED LINEAR WALL GUIDES LED GUIDE - WARM WHITE, DIMMABLE ZONE A: COVE/RECESSED	
	FLUTED WOOD PANEL LED STRIP BEHIND FLUTED PANELS - WARM GLOW	
	INTEGRATED RECESSED LED STRIP BEHIND PANEL - WARM GLOW ZONE B: 15'	
	ADJUSTABLE SPHERICAL AMBER GLASS PENDANTS - WARM CRI ZONE B: (SET OF 2)	
	INTEGRATED RGBWW WARM WHITE LED BACKLIGHTING PANEL - CONTROLLED VIA APP ZONE D: 180W	
	INTEGRATED LINEAR MIRROR LIGHTS - FRONT TASK LIGHTING ZONE A: RECESSED ZONE B: DECORATIVE WALL ZONE C: TASK	
	WARDROBE INTERIOR LIGHTS ZONE A: AUTO SENSOR ZONE D: ZONE D: FEATURE BACKLIGHT ZONE C: TASK	
	RECESS KICKPLATE LED STRIP LIGHTING ZONE A: 3500K ZONE B: 30W	
LEGEND  ZONE A (TEAL): SLEEP  ZONE B (BEIGE): DRESSING  ZONE C (GOLD): MEDIA  ZONE D (MOSS GREEN): RELAXATION  PATH (CLEAR): CIRCULATION		
PROFESSIONAL		
PROFESSIONAL		
DATE	SCALE	TITLE
01-09-2023	1:50	1

indeva
Studio

SPATIAL ZONING PLAN

MATERIAL SPECIFICATIONS & JOINERY DETAILS

MATERIAL BOARD

- Fluted MDF – vertical profile, 18 mm
- Edge band – 2 mm ABS, color-matched
- Plywood – 18 mm MR, BWP grade
- PU finish – 2 coats primer, 2 coats topcoat
- Brass hardware – PVD brushed finish

HARDWARE SCHEDULE

Blum hinges, Hettich drawer channels, aluminum LED profiles, concealed fixings throughout.



BED FEATURE WALL

The bed wall is conceived as the spatial anchor of the room — a composition of vertical fluted walnut panelling, upholstered headboard, and concealed LED strip lighting that creates depth and warmth.

FEATURE WALL & HEADBOARD

Overall width: 3060 mm · Headboard zone: 2360 mm centred
Upholstered fabric · 50mm foam · 18mm ply base · 600mm height

FLUTED WALNUT PANEL

12mm thick · Warm white LED strip (3000K) integrated behind panel reveals Fluted
MDF detail: 18mm · PU finish · 120mm module width

BEDSIDE TABLES & FINISH

PU finish with metal frame · Concealed LED strip (3000K) beneath
Skirting: MS hairline finish · Wall paint: warm white

PLANNING NOTES

King bed centered on main wall – min. 900 mm circulation clearance

TV unit opposite bed at optimal viewing distance

Wardrobe with full-opening doors – 1000 mm clear zone

Dressing unit adjacent to wardrobe with integrated mirror

Window seat with under-seat storage

📏 All dimensions in millimetres. Verify site conditions before fabrication.



NOTES

- ALL DIMENSIONS ARE IN MM.
- ALL FINISHES AS PER MATERIAL BOARD.
- LED STRIP LIGHT - WARM WHITE (3000K).
- CONCEALED LIGHTING IN FLUTED WALNUT PANEL.
- WALL SCONCES CENTERED IN LED FRAME PANELS.





indéva
Studio

TV UNIT & ENTERTAINMENT WALL WORKING DRAWING MATERIAL DETAILS

DIMENSIONS

Overall width: **2030 mm** · Height: **2050 mm** · TV back panel height: **1200 mm**

TV BACK PANEL

Calacatta marble look panel (PU finish) · TV as per client selection

CARCASS & DRAWERS

18mm PLY + laminate · Drawers: 18mm PLY + PU finish, warm beige

FLUTED PANEL & LED


15mm MDF + PU finish · Calacatta marble look
LED strip: warm white (3000K) · Aluminium LED profile

HARDWARE

Handle: brass finish · Knob: walnut, brass / Calacatta marble look
12mm fluted walnut panel · 10mm PLY backboard



Integrated storage and clean joinery detailing eliminate visual clutter; warm backlighting reinforces the room's ambient lighting hierarchy.

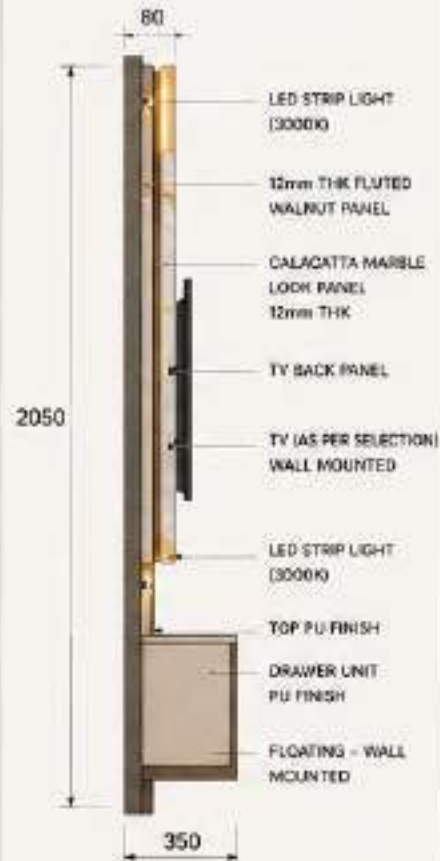

SPECIFICATIONS

- CARCASS: 18mm PLY + LAMINATE
- DRAWERS: 18mm PLY + PU FINISH
- FLUTED PANEL: 12mm MDF + PU FINISH
- BACK PANEL: 12mm THK CALACATTA MARBLE LOOK PANEL
- HANDLE: BRASS KNOB
- LED STRIP: WARM WHITE (3000K)
- FINISH: PU PAINT - MATTE
- COLOR: WARM BEIGE, WALNUT, BRASS, CALACATTA MARBLE LOOK



4. TV UNIT ELEVATION




NOTES

- ALL DIMENSIONS ARE IN MM.
- ALL FINISHES AS PER MATERIAL BOARD.
- PROVIDE 2" GAP BEHIND TV BACK PANEL FOR WIRING & VENTILATION.
- LED STRIP LIGHT TO BE CONCEALED IN ALUMINIUM PROFILE.
- DRAWERS & SHUTTERS TO BE SOFT CLOSE.

5. LED DETAIL (SECTION)



6. FLUTED PANEL DETAIL

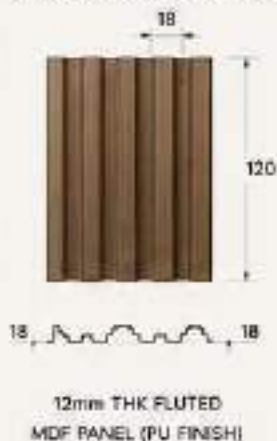

7. HANDLE DETAIL



SOLID BRASS KNOB

8. REFERENCE IMAGE





indéva
Studio

OPTION 1



indéva
Studio

OPTION 2

DRESSING UNIT

The wardrobe and dressing unit are designed as a unified storage wall — combining generous hanging space, internal organisation, and a dedicated vanity with LED-lit mirror.

WARDROBE

Width: **2400 mm** · Height: **2760 mm** · 4 shutter leaves · 600mm module
Carcass: 18mm PLY + laminate · Shutters: 18mm PLY + PU matte, warm beige / light taupe

INTERNAL ORGANISATION

Long hang: 1050mm · Short hang: 450mm · Shelves · Drawers: 510mm
Soft-close telescopic hinges · Brass finish long handle & knob

DRESSING UNIT & MIRROR

Width: **1100 mm** · LED strip (3000K) around mirror · Fluted MDF panel, PU finish
Mirror: 6mm thick · LED-lit surround · Clear gap detail · Brass finish handle · Soft-close drawer channel


STOOL

Upholstered, gold finish base · 450 × 450 mm


1. DRESSING UNIT ELEVATION (FRONT VIEW)



2. SIDE ELEVATION (SECTION)

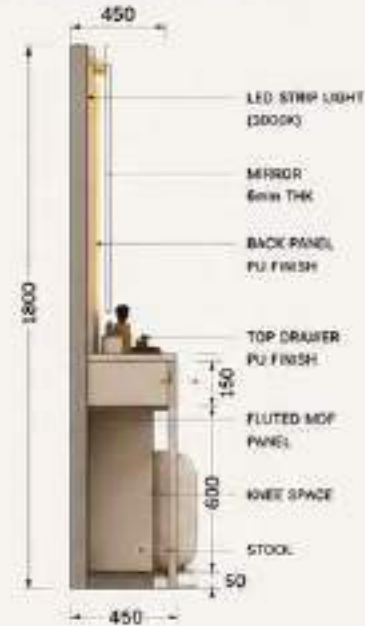

3. PLAN VIEW (TOP)

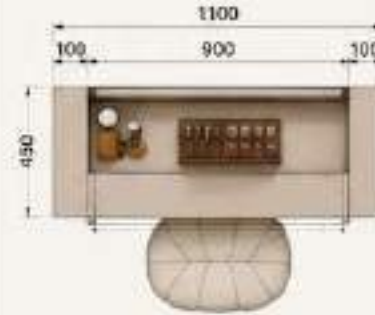

SPECIFICATIONS

- CARCASS : 18mm PLY + LAMINATE
- DRAWER : 18mm PLY + PU FINISH
- FLUTED PANEL : 18mm MDF + PU FINISH
- HANDLE : BRASS FINISH
- MIRROR : 6mm THK WITH LED LIGHT
- FINISH : PU PAINT - MATTE
- COLOR : WARM BEIGE

MATERIAL & FINISH PALETTE




indéva
Studio

Dressing Unit Wall Working Drawing


4. DRAWER INTERNAL LAYOUT



5. FLUTED PANEL DETAIL

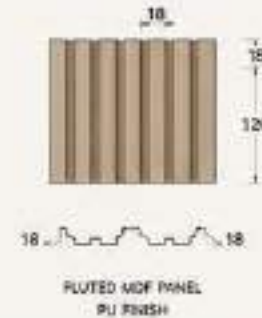

6. MIRROR & LED DETAIL (SECTION)

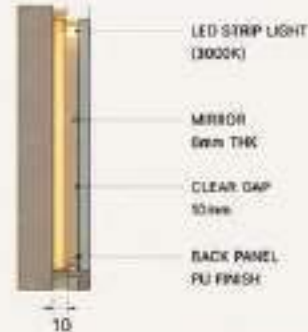

7. STOOL



NOTES

- ALL DIMENSIONS ARE IN MM.
- ALL FINISHES AS PER MATERIAL BOARD.
- LED STRIP LIGHT - WARM WHITE (3000K).
- PROVIDE SA SOCKET BEHIND MIRROR FOR APPLIANCES.
- DRAWER & SHUTTERS TO BE SOFT CLOSE.





indéva
Studio

WINDOW SEAT & JOINERY DETAILS

DIMENSIONS

Overall width: **1950 mm** · Height: **2200 mm** · Seat depth: **600 mm**

SEAT CUSHION

Fabric upholstery · 50mm TK foam · 18mm ply base · Soft-close shutter channel


OPEN DISPLAY SHELVES

PU finish · LED strip light (3000K) integrated · Warm beige finish

STORAGE & DRAWERS

Below seat: shutter PU finish · Soft-close channel · Brass finish handle
Drawers: PU finish with brass handle

Bay Window Wall Working Drawing

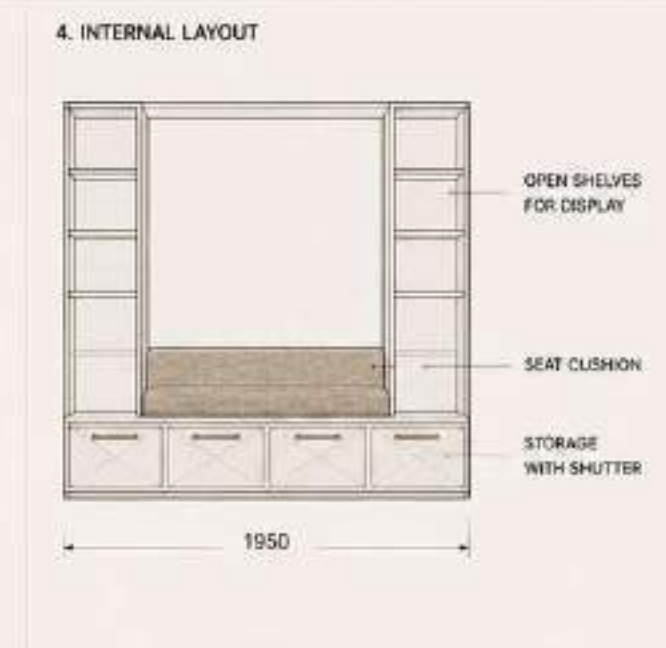

Cozy & Modern Bay Window Nooks





VERTICAL FLUTED WALNUT PANEL WITH LED STRIP

WALL LIGHT

PU PANEL WARM BEIGE

UPHOLSTERED HEADBOARD

BEDSIDE TABLE WITH BRASS DETAIL

OPEN DISPLAY WITH WARM LED

CALACATTA MARBLE LOOK BACK PANEL

TV UNIT (FLOATING)

BRASS HARDWARE



indéva
Studio



- Double hanging – 1700 mm clear height
- Drawer bank – 6 drawers, full-extension channels
- Loft storage – 450 mm above hanging rail
- Shoe shelves – adjustable, 300 mm depth
- Mirror panel – full-height, sliding door

Walnut veneer doors, brushed brass handles, MR plywood carcass, matte PU interior

COMPLETE ROOM EXPERIENCE

indéva
Studio



FUNCTIONALITY

Every element — wardrobe, dressing unit, window seat, TV wall — is designed to serve a precise function without visual compromise.

COMFORT

Upholstered surfaces, warm lighting, and generous proportions create a room that is as comfortable as it is considered.

LIGHTING

Layered strategy — cove, recessed, strip, and pendant — allows the room to transition seamlessly from day to evening.

MATERIAL HARMONY

Walnut, beige, brass, and white read as a single, cohesive palette across all four walls.

SPATIAL BALANCE

Symmetrical bedwall, balanced storage distribution, and a clear circulation path ensure the room feels ordered and calm at every vantage point.



indéva
Studio

FINAL DESIGN SUMMARY

The Parents Bedroom at Vasant Kunj

A carefully curated material palette of walnut fluting, warm beige lacquer, Calacatta marble accents, and brushed brass hardware creates an interior of quiet sophistication.

Integrated lighting—layered across cove, panel, and pendant sources—allows the room to shift in mood from the clarity of morning to the intimacy of evening.

Clean joinery reinforces architectural simplicity; balanced proportions ensure timeless elegance. Every detail, from the fluted headboard wall to the brass drawer pull, is resolved with the same rigour and restraint.

The result is a bedroom that does not announce itself—it simply envelops.

"Designed for comfort, understated luxury, and everyday living."

FINAL VISUALIZATION & EXECUTION NOTES

INSTALLATION

Sequence: ceiling → walls → flooring → joinery → lighting → upholstery. Protect finished surfaces at each stage.

QUALITY STANDARDS

Tolerances: $\pm 2\text{mm}$ for joinery, $\pm 3\text{ mm}$ for stone. All hardware tested before handover.

KEY SPECIFICATIONS

All dimensions in mm. Verify site conditions. Submit shop drawings before fabrication.

